


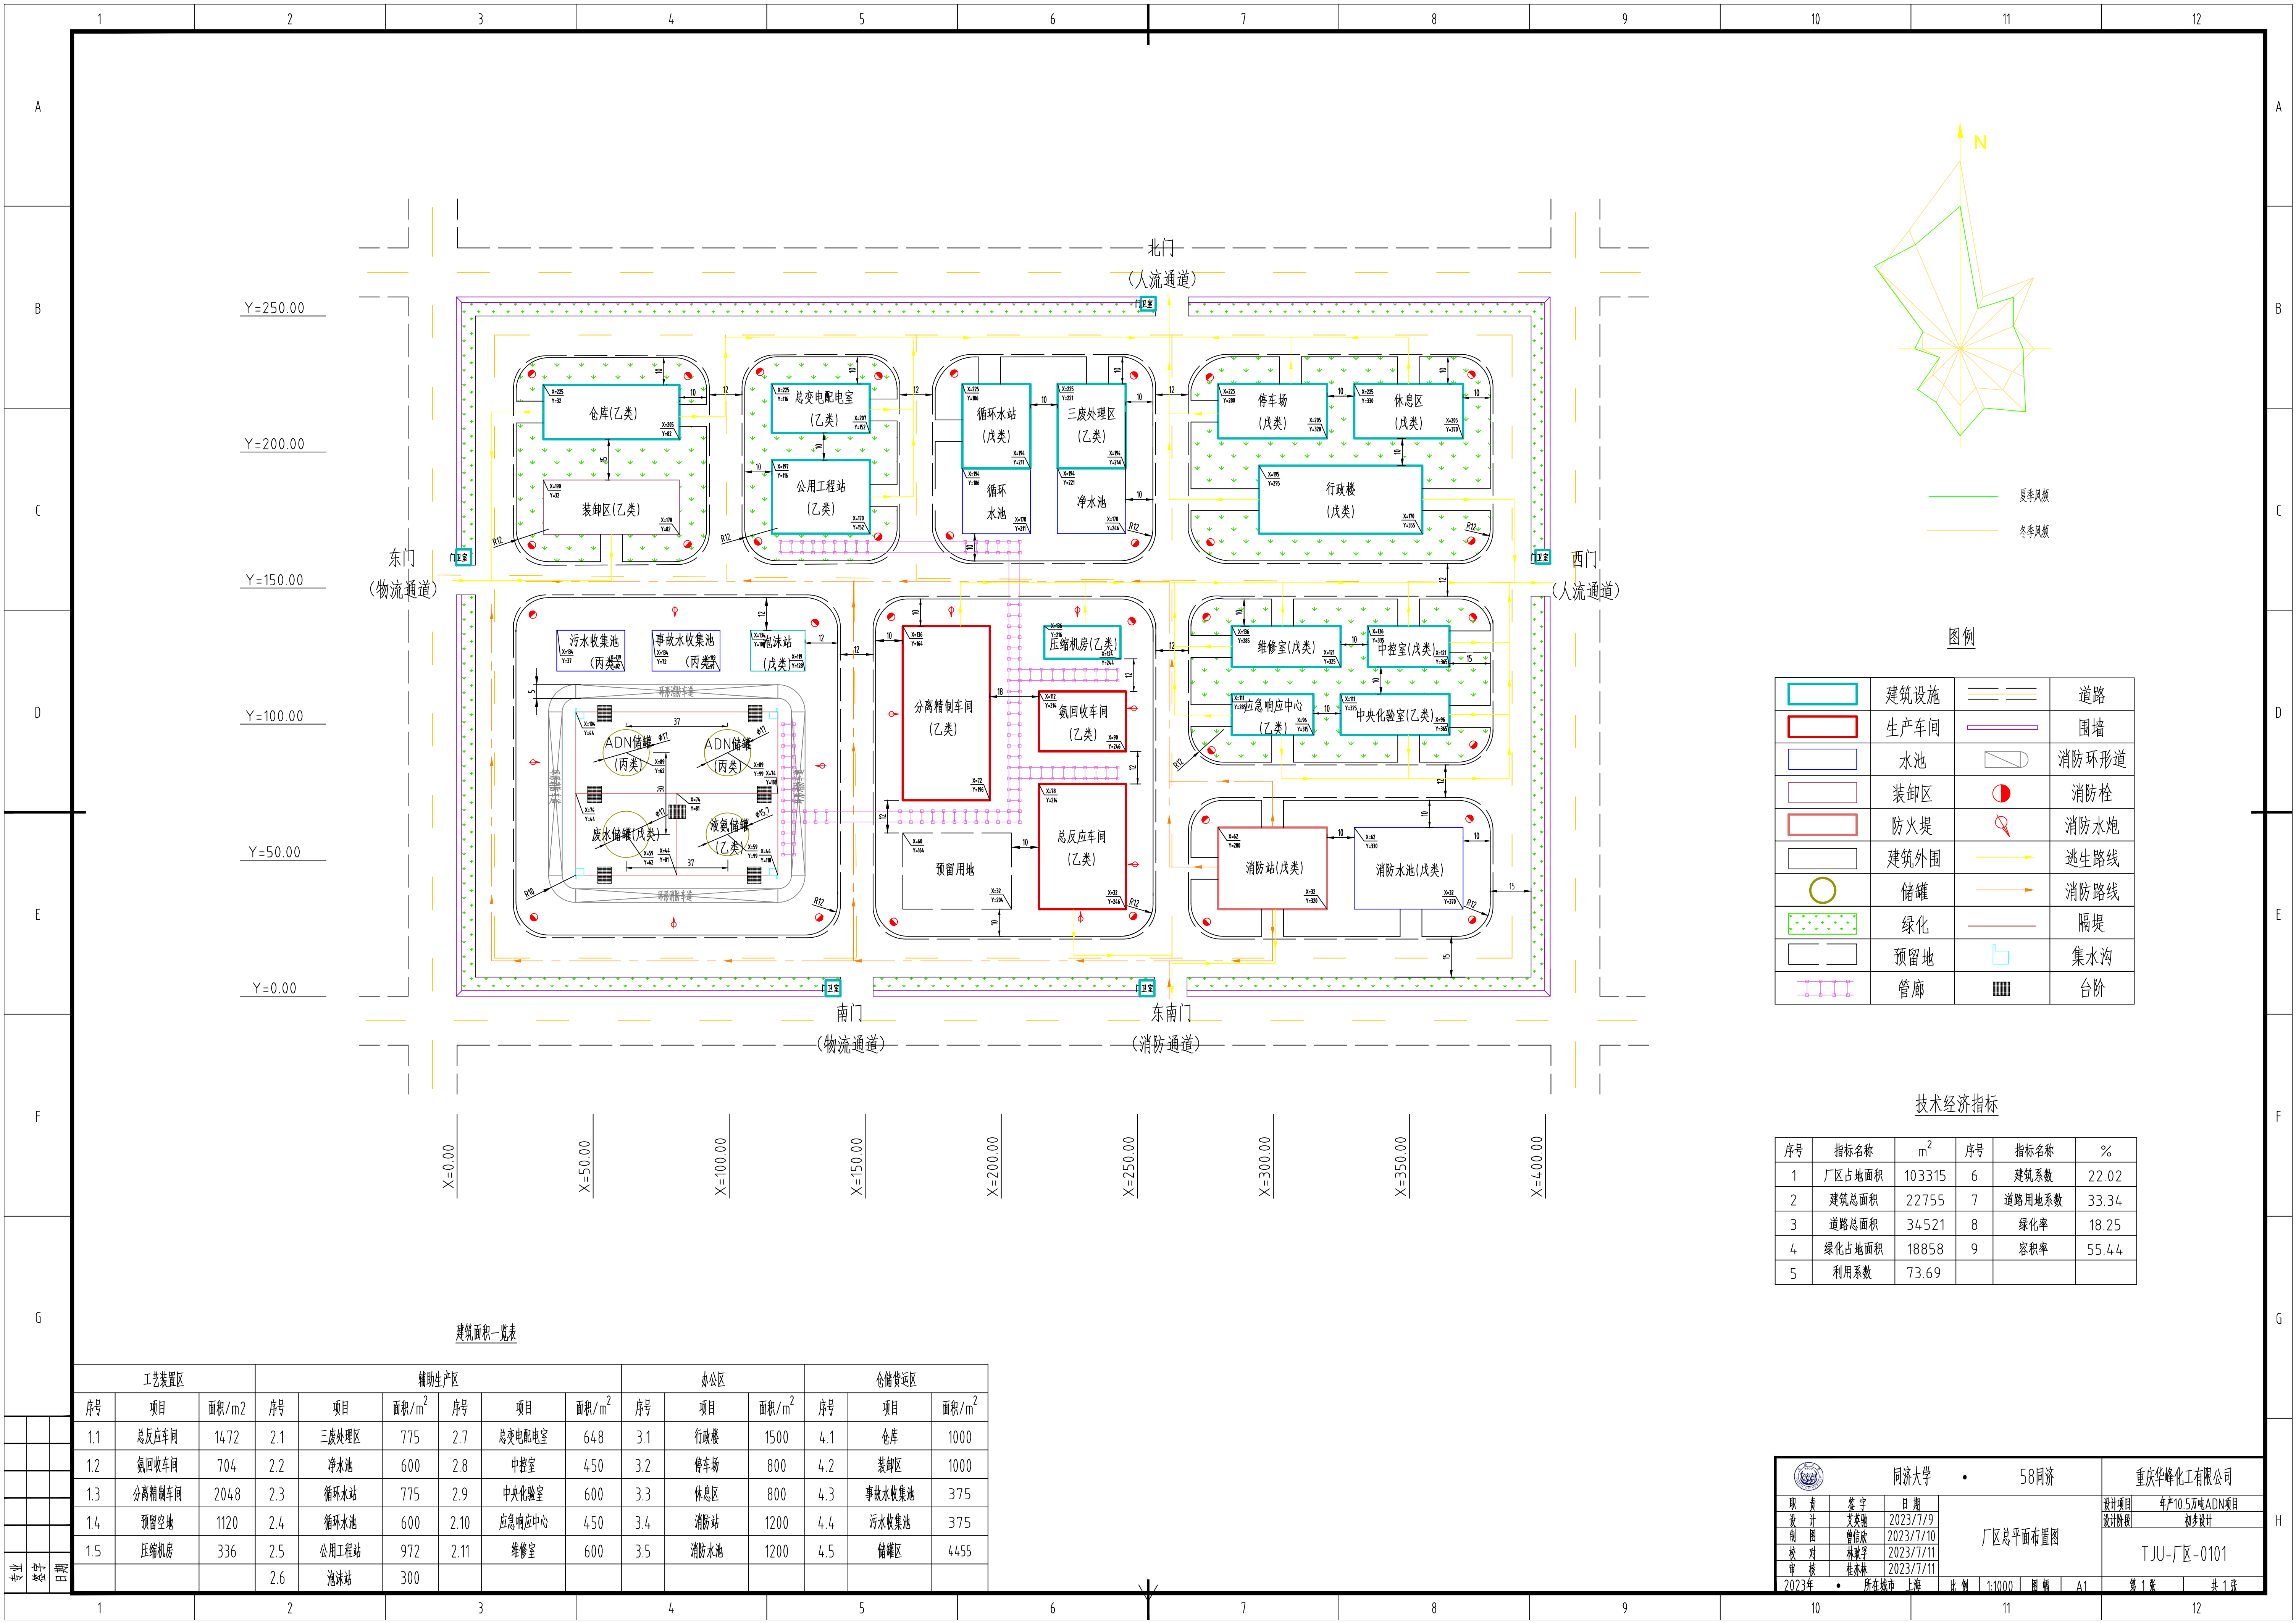

	建筑设施		道路
	生产车间		围墙
	水池		消防环形道
	装卸区		消防栓
	防火堤		消防水炮
	建筑外围		逃生路线
	储罐		消防路线
	绿化		隔堤
	预留地		集水沟
	管廊		台阶

技术经济指标

序号	指标名称	m ²	序号	指标名称	%
1	厂区占地面积	103315	6	建筑系数	22.02
2	建筑总面积	22755	7	道路用地系数	33.34
3	道路总面积	34521	8	绿化率	18.25
4	绿化占地面积	18858	9	容积率	55.44
5	利用系数	73.69			

建筑面积一览表

工艺装置区			辅助生产区			办公区			仓储货运区		
序号	项目	面积/m ²	序号	项目	面积/m ²	序号	项目	面积/m ²	序号	项目	面积/m ²
1.1	总反应车间	1472	2.1	三废处理区	775	2.7	总变配电室	648	3.1	行政楼	1500
1.2	氨回收车间	704	2.2	净水池	600	2.8	中控室	450	3.2	停车场	800
1.3	分离精制车间	2048	2.3	循环水站	775	2.9	中央化验室	600	3.3	休息区	800
1.4	预留空地	1120	2.4	循环水池	600	2.10	应急响应中心	450	3.4	消防站	1200
1.5	压缩机房	336	2.5	公用工程站	972	2.11	维修室	600	3.5	消防水池	1200
			2.6	泡沫站	300						

同济大学 · 58同济			重庆华峰化工有限公司	
设计	签字	日期	厂区总平面布置图	设计项目
设计	艾美露	2023/7/9		年产10.5万吨ADN项目
校核	曾信成	2023/7/10		初步设计
审核	林晓宇	2023/7/11		TJU-厂区-0101
审核	桂永林	2023/7/11	所在城市 上海	
比例 1:1000 图幅 A1			第 1 页	共 1 页