


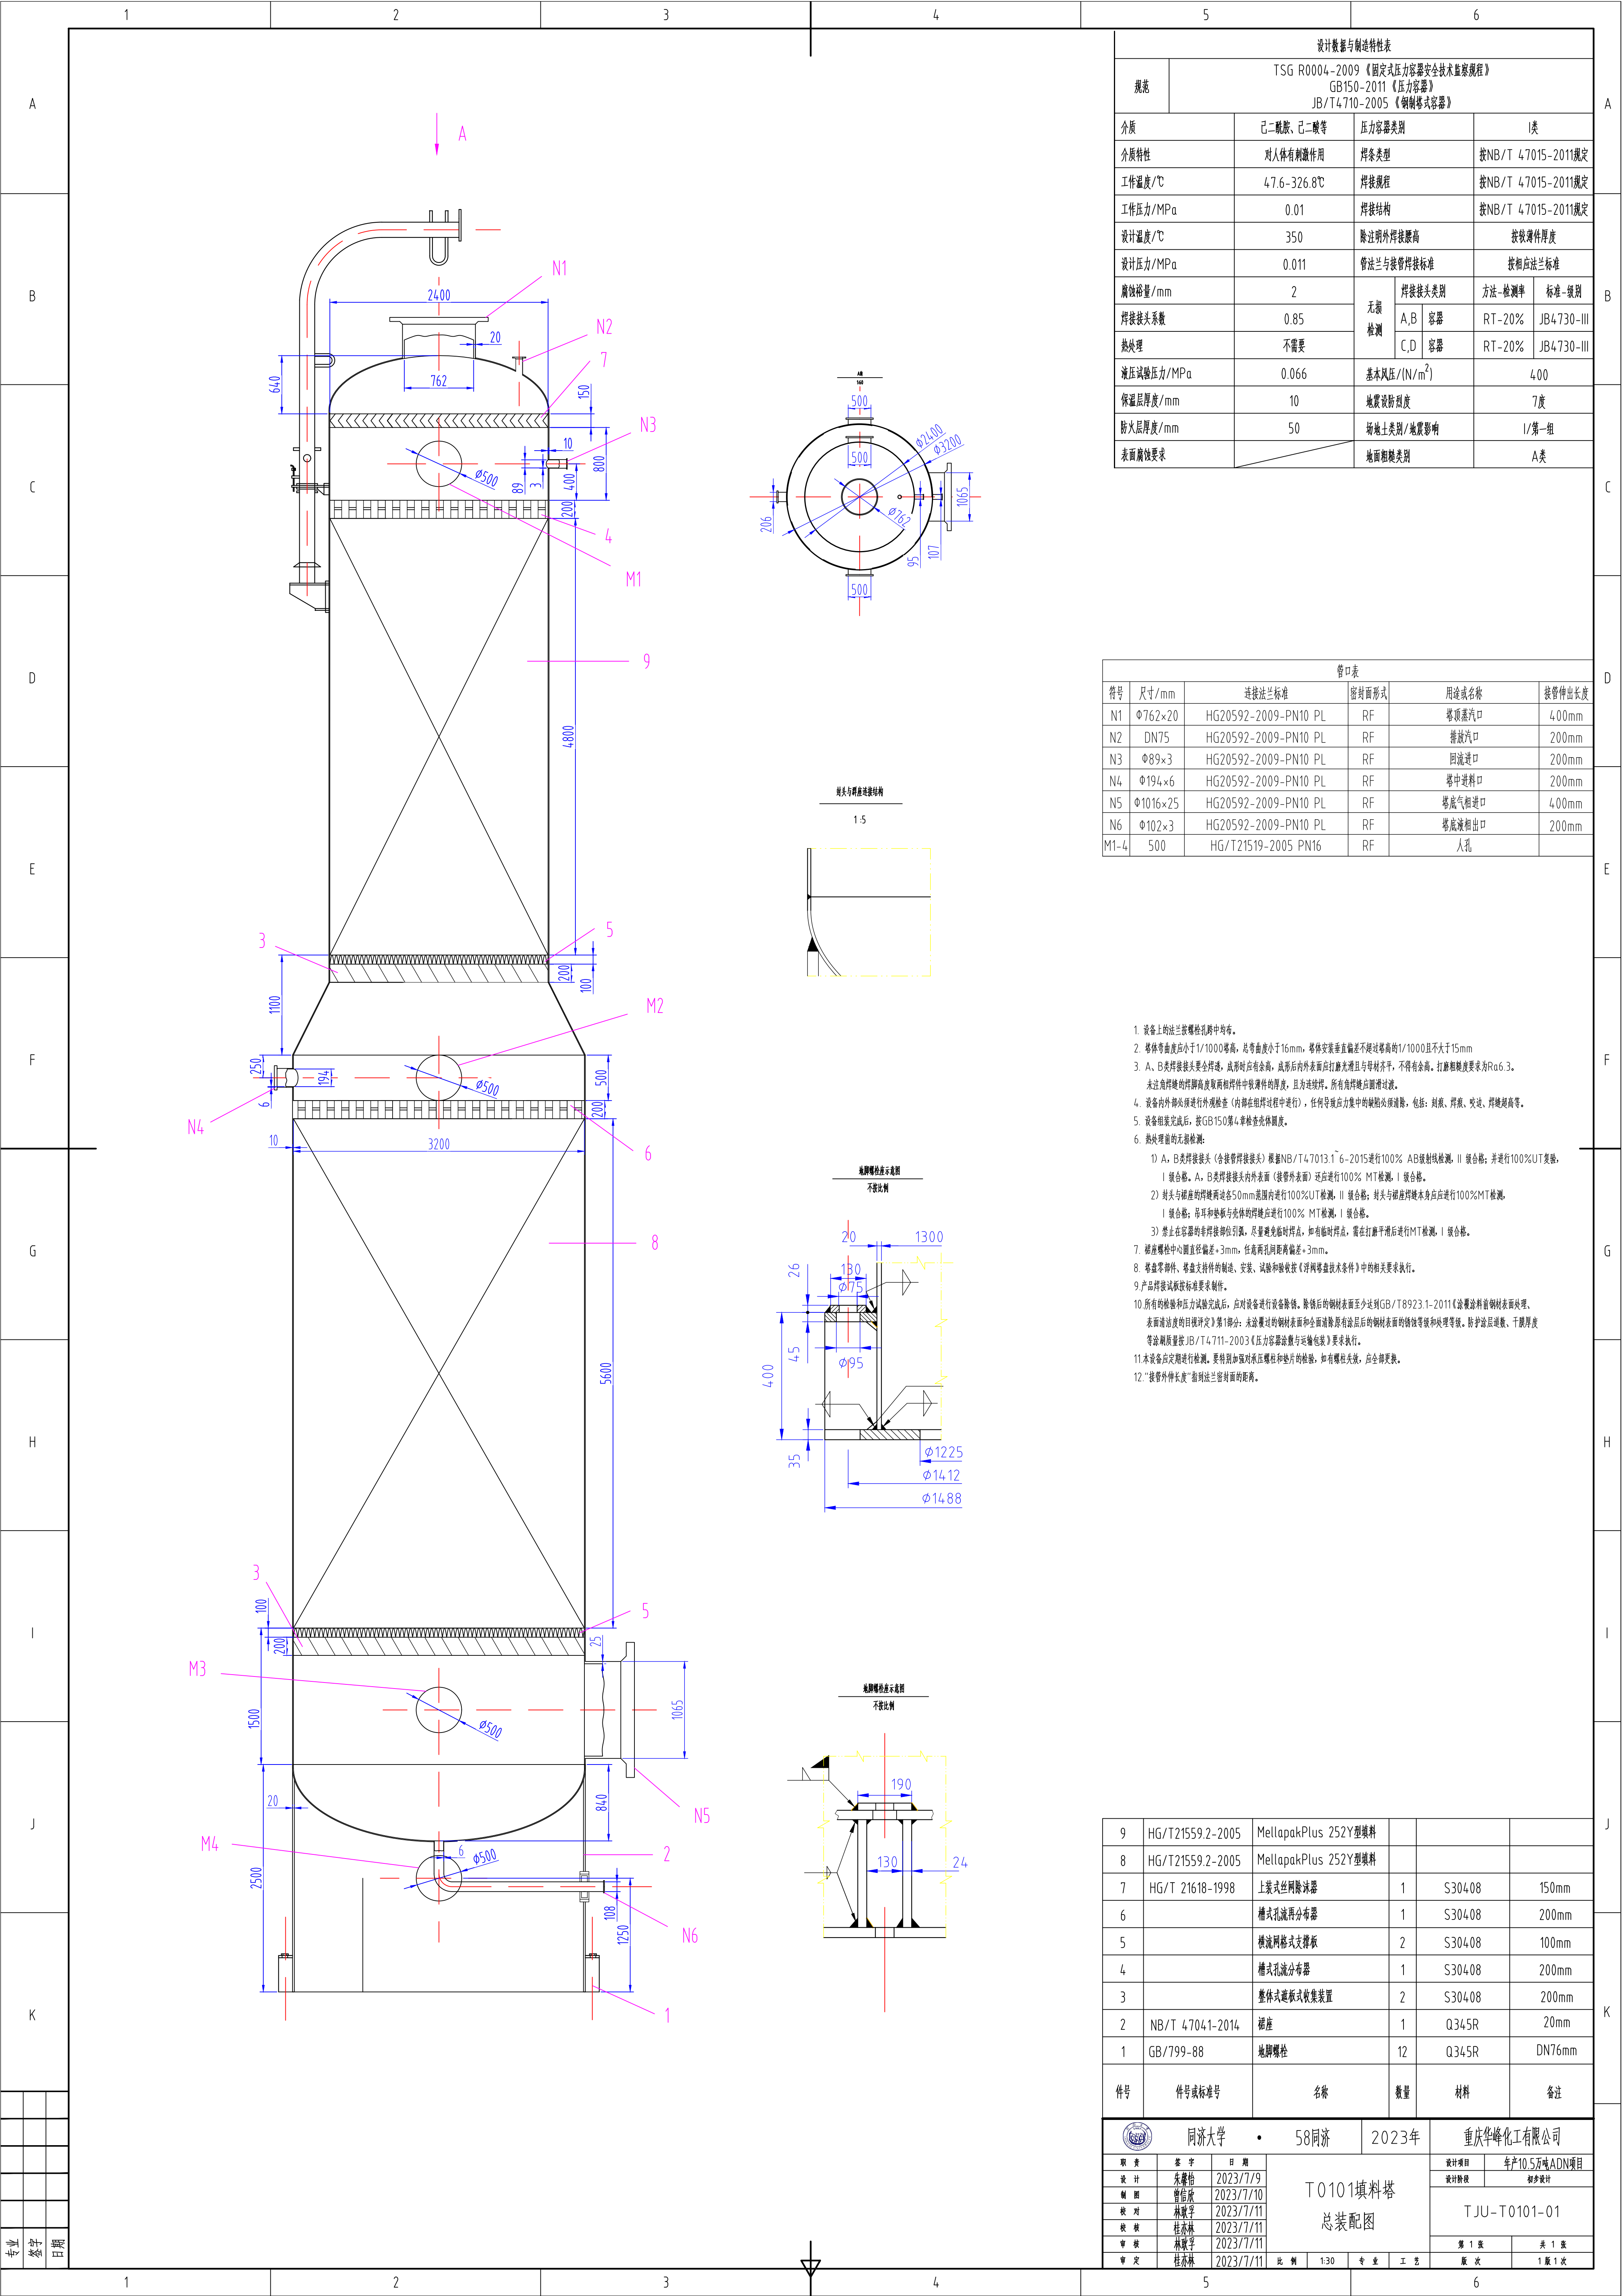

设计数据与制造特性表				
规范	TSG R0004-2009 《固定式压力容器安全技术监察规程》 GB150-2011 《压力容器》 JB/T4710-2005 《钢制塔式容器》			
	介质	己二酰胺、己二酸等	压力容器类别	I类
介质特性	对人体有刺激作用	焊缝类型	按NB/T 47015-2011规定	
工作温度/℃	47.6-326.8℃	焊接规程	按NB/T 47015-2011规定	
工作压力/MPa	0.01	焊接结构	按NB/T 47015-2011规定	
设计温度/℃	350	除注明外焊接要求	按较薄件厚度	
设计压力/MPa	0.011	管法兰与接管焊接标准	按相应法兰标准	
腐蚀裕量/mm	2	无损检测	焊接接头类别	方法-检测率
焊接接头系数	0.85		A,B 容器	RT-20%
热处理	不需要		C,D 容器	RT-20%
液压试验压力/MPa	0.066	基本风压/(N/m ²)	400	
保温层厚度/mm	10	地震设防烈度	7度	
防火层厚度/mm	50	场地土类别/地震影响	I/第一组	
表面腐蚀要求		地面粗糙类别	A类	

管口表					
符号	尺寸/mm	连接法兰标准	密封面形式	用途或名称	接管伸出长度
N1	Φ762×20	HG20592-2009-PN10 PL	RF	塔顶蒸汽口	400mm
N2	DN75	HG20592-2009-PN10 PL	RF	排放汽口	200mm
N3	Φ89×3	HG20592-2009-PN10 PL	RF	回流进口	200mm
N4	Φ194×6	HG20592-2009-PN10 PL	RF	塔顶进料口	200mm
N5	Φ1016×25	HG20592-2009-PN10 PL	RF	塔底气相进口	400mm
N6	Φ102×3	HG20592-2009-PN10 PL	RF	塔底液相出口	200mm
M1-4	500	HG/T21519-2005 PN16	RF	人孔	

1. 设备上的法兰按螺栓孔距中分布。
2. 塔体等直度应小于1/1000塔高，总弯曲度应小于16mm，塔体安装垂直偏差不得超过塔高的1/1000且不得大于15mm。
3. A、B类焊接接头要全焊透，成形时应有余高，成形后的外表面应打磨光滑且与母材齐平，不得有缺陷。打磨粗糙度要求为Ra6.3。
- 未注角焊缝的焊脚高度取两相焊件中较薄件的厚度，且为连续焊。所有角焊缝应圆滑过渡。
4. 设备内外表面须进行外观检查（对缺陷在制造过程中进行），任何导致应力集中的缺陷必须消除，包括：划痕、焊痕、咬边、焊缝起高等。
5. 设备组焊完成后，按GB150第4章检查壳体圆度。
6. 热处理后的无损检测：

1) A、B类焊接接头（含接管焊接接头）根据NB/T47013.1~6-2015进行100% AB级射线检测，II级合格；并进行100%UT复验，I级合格。A、B类焊接接头内外表面（接管外表面）还应进行100% MT检测，I级合格。

2) 封头与裙座的焊缝按各50mm范围进行100%UT检测，II级合格；封头与裙座焊缝本身应进行100%MT检测，I级合格；吊耳和垫板与壳体的焊缝应进行100% MT检测，I级合格。

3) 禁止在容器的非焊接部位引弧，尽量避免临时焊点，如有临时焊点，需在打磨平滑后进行MT检测，I级合格。
7. 裙座螺栓中心圆直径偏差+3mm，任意两孔间距离偏差+3mm。
8. 塔盘零部件、塔盘支撑件的制造、安装、试验和验收按《浮阀塔盘技术条件》中的相关要求执行。
9. 产品焊接试板按标准要求制作。
10. 所有的检验和压力试验完成后，应对设备进行设备除锈，除锈后的钢材表面至少达到GB/T8923.1-2011《涂覆涂料前钢材表面处理、表面清洁度的目视评定》第1部分：未涂覆过的钢材表面和全面清除原有涂层的钢材表面的锈蚀等级和处理等级，防护涂层道数、干膜厚度等涂膜质量按JB/T4711-2003《压力容器涂敷与运输包装》要求执行。
11. 本设备应定期进行检测，要特别加强对承压螺栓和垫片的检验，如有螺栓失效，应全部更换。
12. “接管外伸长度”指到法兰密封面的距离。

9	HG/T21559.2-2005	MellapakPlus 252Y型填料			
8	HG/T21559.2-2005	MellapakPlus 252Y型填料			
7	HG/T 21618-1998	上装式丝网除沫器	1	S30408	150mm
6		槽式孔流再分布器	1	S30408	200mm
5		横流网格式支撑板	2	S30408	100mm
4		槽式孔流分布器	1	S30408	200mm
3		整体式遮蔽式收集装置	2	S30408	200mm
2	NB/T 47041-2014	裙座	1	Q345R	20mm
1	GB/799-88	地脚螺栓	12	Q345R	DN76mm
件号	件号或标准号	名称	数量	材料	备注

		同济大学		•	58同济		2023年		重庆华峰化工有限公司		
负责人	签字	日期		T0101填料塔 总装配图							
设计	朱耀怡	2023/7/9									
制图	曹信欣	2023/7/10									
校对	林敏宇	2023/7/11									
审核	桂永林	2023/7/11									
审定	林敏宇	2023/7/11									
				比例	1:30	专业	工 艺	版 次			
				第 1 张							共 1 张
								1 版 1 次			