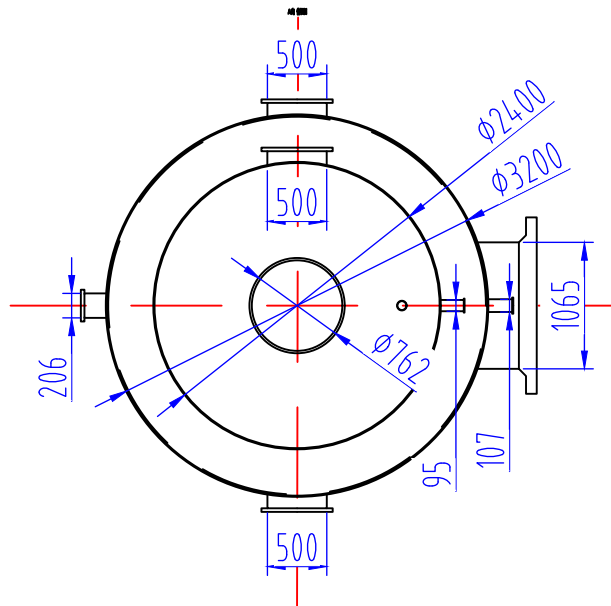
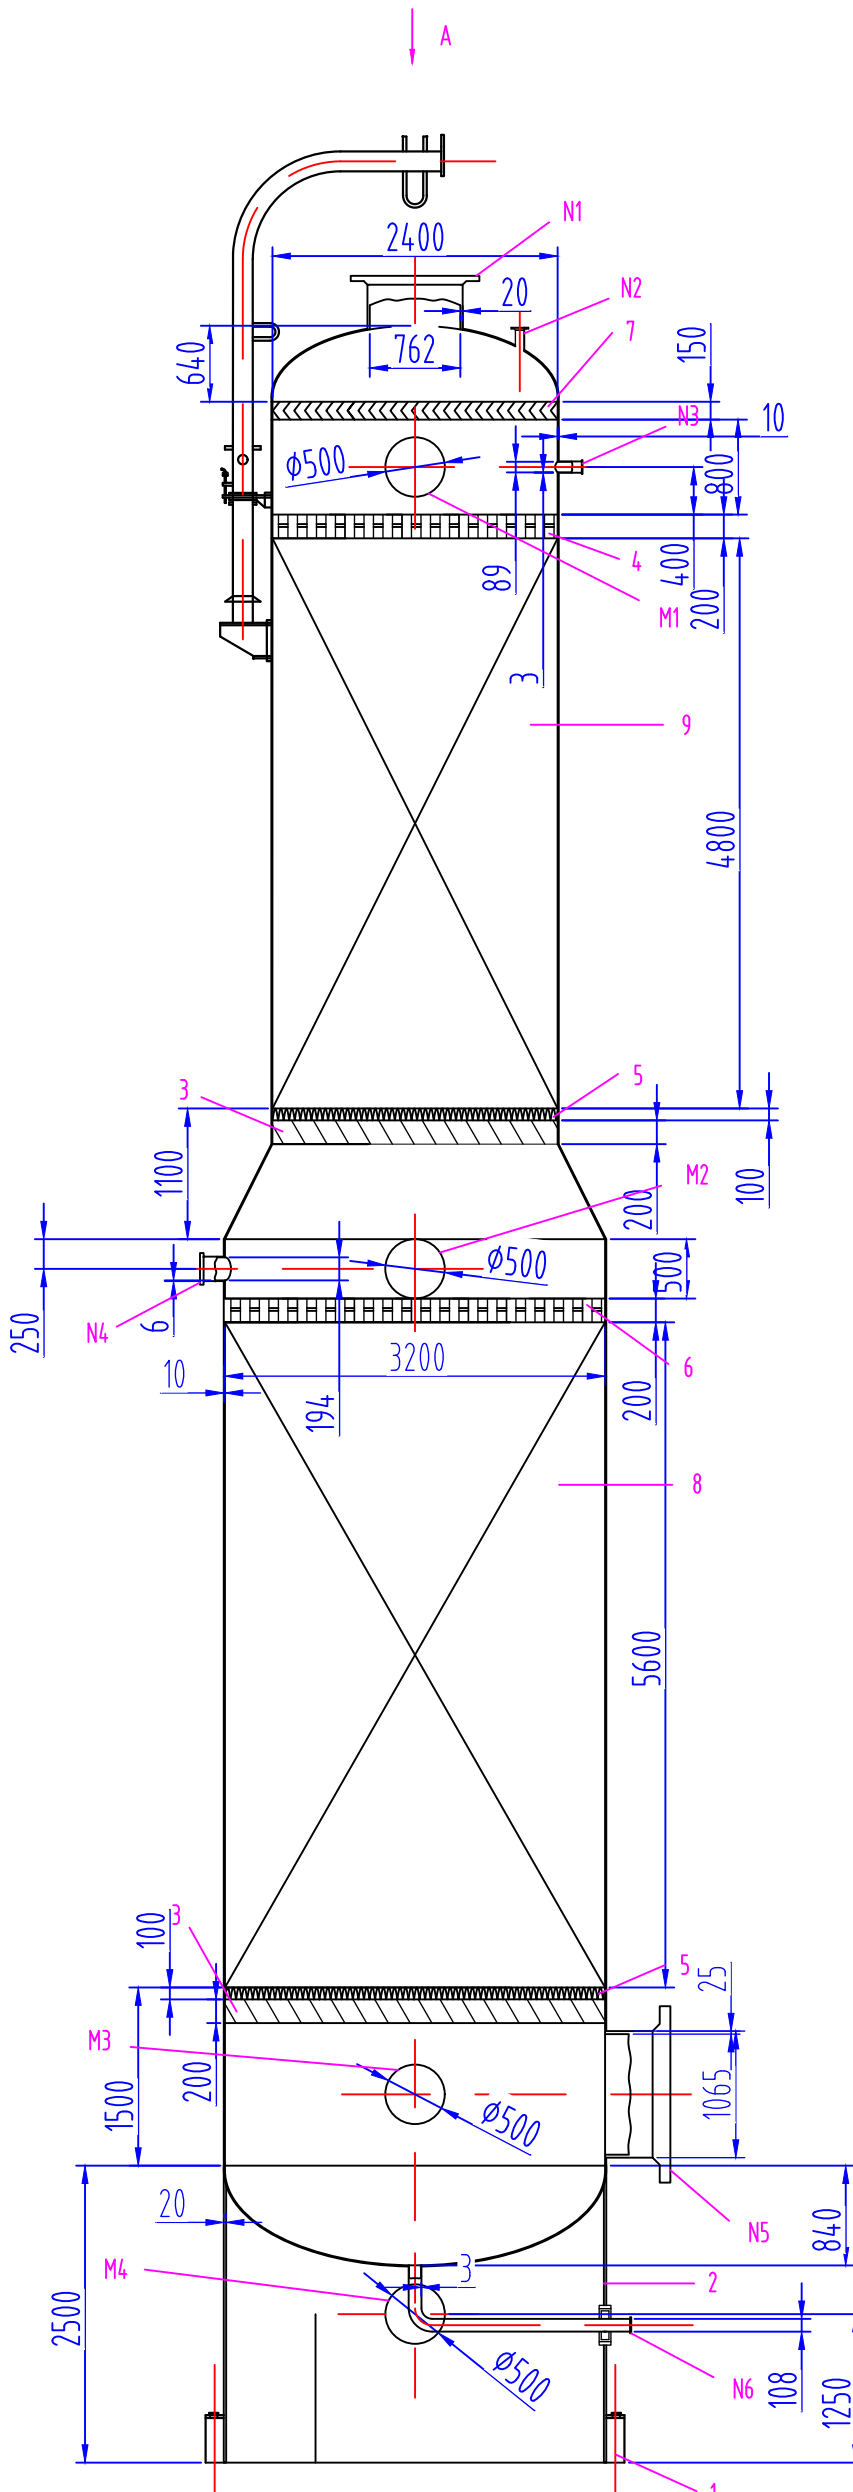


		同济大学 • 58同济		重庆华峰化工有限公司		塔设备工艺条件图		编 制	艾英驰	2023/7/9	设计阶段	初步设计
		年产10.5万吨ADN项目		TJU-塔设备-T0101				校 核	曾信欣	2023/7/10	第1张 / 共1张	
								审 核	林耿孚	2023/7/11		
1	操作压力 (MPa)		0.01		位号	T0305	设备名称		差压精馏塔			
2	操作温度 (塔顶/塔釜) (℃)		47.6/326.8		塔型	填料塔	内径X塔高 (mm)		700X17700			
3	壳体材料及腐蚀裕度 (mm)		2		符 号	直径/mm	法兰标准	连接面	用途			
4	内件材料 (推荐)		S30408									
5	衬里防腐要求		/		N1	Φ762×20	HG/T20592-2009	SW-RF	塔顶蒸汽口			
6	物料名称		己二酰胺、己二酸等		N2	DN75	HG/T20592-2009	SO-RF	排放气口			
7	进料量 (m³/h)		1886.9		N3	Φ89×3	HG/T20592-2009	SW-RF	回流进口			
8	气体比重 (kg/m³)		0.0677		N4	Φ194×6	HG/T20592-2009	SW-RF	塔中进料口			
9	液体比重 (kg/m³)		0.9323		N5	Φ1016×25	HG/T20592-2009	SW-RF	塔底气相进口			
10	液体喷洒量		/		N6	Φ102×3	HG/T20592-2009	SW-RF	塔底液相出口			
11	填料容积 (m³)		2.17/5.02		M1	500	HG/T20592-2009	SO-RF	人孔			
12	填料比重 (kg/m³)		88.32		M2	500	HG/T20592-2009	SO-RF	人孔			
13	填料规格		规整填料MellapakPlus™ 252Y		M3	500	HG/T20592-2009	SO-RF	人孔			
14	填料排列方式		规整		M4	500	HG/T20592-2009	SO-RF	人孔			
15	汽液分离要求		丝网除沫器		说明: 1、设备需静接地; 2、管口尺寸以此表为准; 3、设置安装平面: ±0.00平面; 4、管口方位以工艺管口方位图为准。							
16	塔板数/板间距		/									
17	筛板孔径/个数/间距		/									
18	浮阀 (泡罩) 规格/个数/间距		/									
19	溢流程数		/									
20	溢流堰高度 两侧/中心 (mm)		/									
21	降液管规格		/									
22	降液管底隙 (mm)		/									
23	液体出口防旋涡要求		/									
24	要求裙座高度 (mm)		2500									
25	安全装置起跳或爆破压力 (MPa)		0.1									
26	保温层厚度		10mm									
27	安全环境及生产类别		乙类									
28	基本风压值 (N/m²)		400									

比例: 1:60